

NAY HOUSE

Pengarengan Blok D No 191 Kelurahan Jatinegara Kecamatan Cakung Jakarta Timur

GAHARU
KONSTRUKSINDO
UTAMA
www.gaharukonstruksindo.com

Grand Galaxy City RSN 1 No. 37, RT.0001 / RW.002, Jaka Setia, Kec. Bekasi Selatan, Kota Bekasi, Jawa Barat 17147

E : gaharukonstruksindo@gmail.com
P : +62 811 – 9409 – 368
I : @renovasirumah_minimalis

NAY HOUSE DESIGN


PT GAHARU KONSTRUKSINDO UTAMA

General Contractor & Interior


DAFTAR GAMBAR

NO	REF	NAMA GAMBAR	SKALA
		COVER	
		DAFTAR GAMBAR	
001	AR - 001	DENAH EKSISTING	
002	AR - 002	DENAH RENCANA LT.1 DAN LT.2	1 : 90
003	AR - 003	DENAH RENCANA LT.3 DAN ATAP	1 : 90
004	AR - 004	TAMPAK DEPAN DAN BELAKANG	1 : 90
005	AR - 005	TAMPAK SAMPING KANAN DAN KIRI	1 : 90
006	AR - 006	DENAH RENCANA PINTU DAN JENDELA LT.1 DAN LT.2	1 : 90
007	AR - 007	DENAH RENCANA PINTU DAN JENDELA LT.3	1 : 90
008	AR - 008	DETAIL PINTU	1 : 40
009	AR - 009	DENAH JENDELA DAN VENTILASI JENDELA	1 : 40
010	AR - 010	DENAH RENCANA POLA LANTAI LT. 1 DAN LT.2	1 : 90
011	AR - 011	DENAH RENCANA POLA LANTAI LT. 3	1 : 90
012	ME - 001	DENAH RENCANA KELISTRIKAN LT.1 DAN LT.2	1 : 90
013	ME - 002	DENAH RENCANA KELISTRIKAN LT.3	1 : 90
014	PLM- 001	DENAH RENCANA AIR BERSIH LT.1 DAN LT.2	1 : 90
015	PLM- 002	DENAH RENCANA AIR BERSIH LT.3	1 : 90
016	PLM- 003	DENAH RENCANA AIR KOTOR LT.1 DAN LT.2	1 : 90
017	PLM- 004	DENAH RENCANA AIR KOTOR LT.3	1 : 90
018	STR - 001	DENAH RENCANA SLOOF DAN PONDASI	1 : 90
019	STR - 002	DETAIL SLOOF DAN PONDASI	1 : 20
020	STR - 003	DENAH RENCANA KOLOM LT.1 DAN LT.2	1 : 90
021	STR - 004	DENAH RENCANA KOLOM LT.3	1 : 90
022	STR - 005	DENAH RENCANA BALOK LT.1 DAN LT.2	1 : 90
023	STR - 006	DENAH RENCANA BALOK LT.3	1 : 90
024	STR - 007	TABEL PENULANGAN KOLOM DAN BALOK	1 : 40
025	STR - 008	DENAH RENCANA PLAT LT.1 DAN LT.2	1 : 90
026	STR - 008	DETAIL PLAT LANTAI LT.2 DAN LT.3	1 : 40

NO	REF	NAMA GAMBAR	SKALA
027	AR - 012	DENAH RENCANA 3D LT.1	NTS
028	AR - 013	DENAH RENCANA 3D LT.2	NTS
029	AR - 014	DENAH RENCANA 3D LT.3	NTS
030	AR - 015	DENAH RENCANA 3D ATAP	NTS
031		EXTERIOR FASAD RUMAH	NTS
032		INTERIOR RUANG KELUARGA DAN DAPUR	NTS
033		RENCANA ANGGARAN BIAYA	

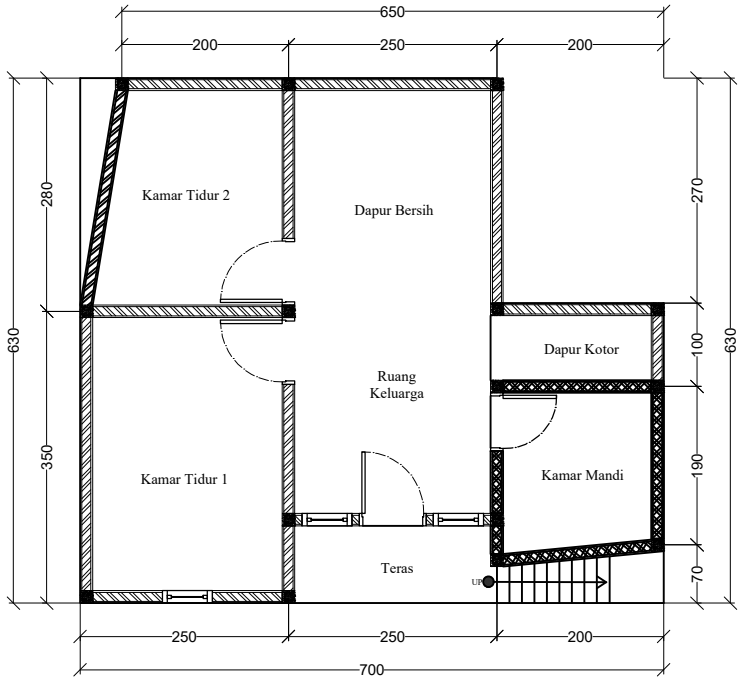

DENAH EKSISTING
SKALA 1:90

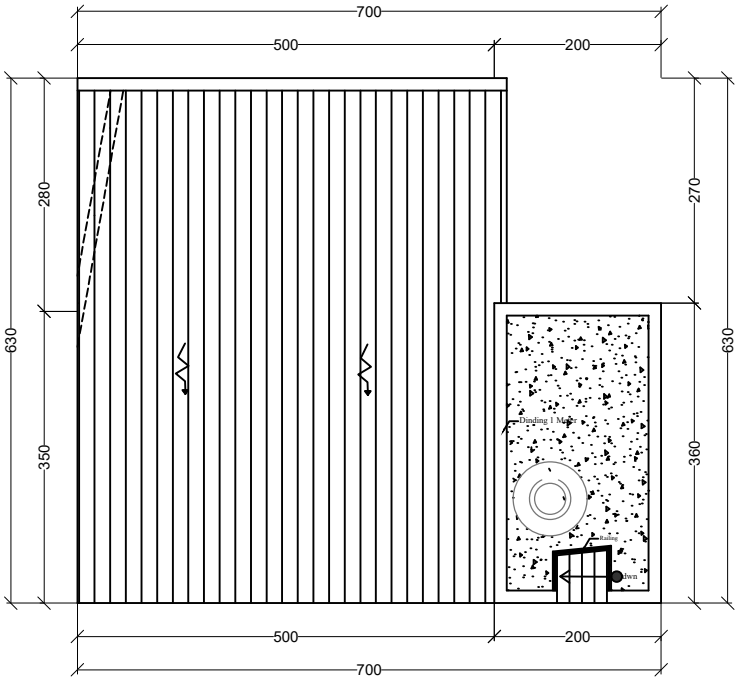

DENAH EKSISTING ATAP
SKALA 1:90

SHOP DRAWING

LEGEND

OWNER

IBU IDA

CONTRACTOR

PT.GAHARU KONSTRUKSINDO UTAMA

DRAWING TITLE

DENAH EKSISTING

DRAWING SCALE

1:90

PROJECT LOCATION

PULO JAHE


APPROVAL BY

PANGGAH NUZHUL RIZKI


DRAWING BY

DYANSHA ALYYA PUTRI

DATE	: 07/10/2022
REVISION	: -
DRAWING CODE	: AR-001
PAGE	: 01

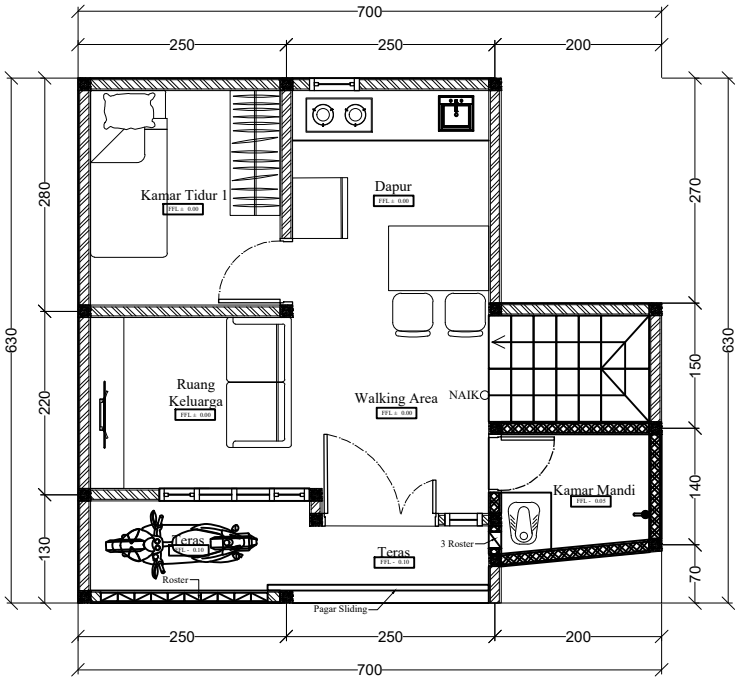

DENAH RENCANA LT. 1
SKALA 1:90

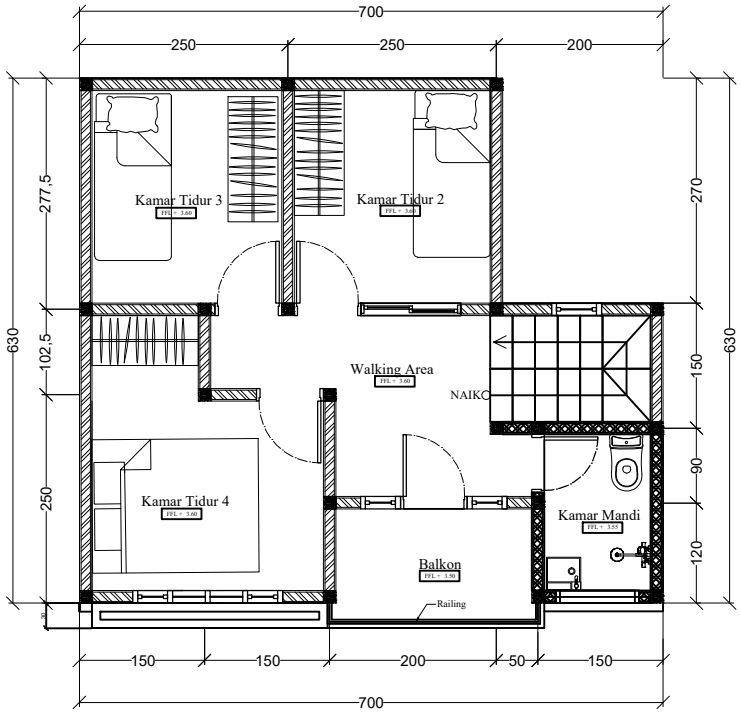

DENAH RENCANA LT. 2
SKALA 1:90

SHOP DRAWING

LEGEND

OWNER

IBU IDA

CONTRACTOR

PT.GAHARU KONSTRUKSINDO UTAMA

DRAWING TITLE

DENAH RENCANA

DRAWING SCALE

1:90

PROJECT LOCATION

PULO JAHE


APPROVAL BY

PANGGAH NUZHUL RIZKI


DRAWING BY

MELA SARI FATONAH

DATE	: 07/10/2022
REVISION	: -
DRAWING CODE	: AR-002
PAGE	: 02

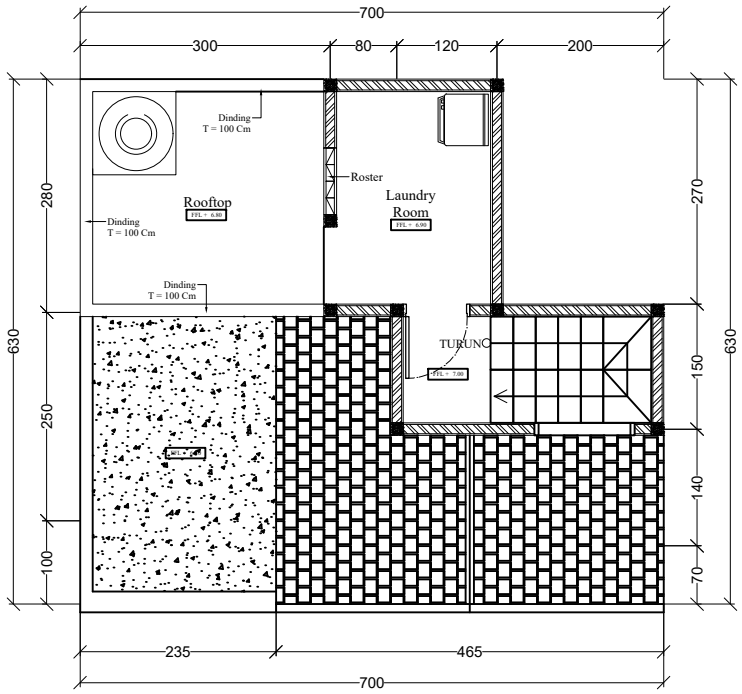

DENAH RENCANA LT. 3
SKALA 1:90

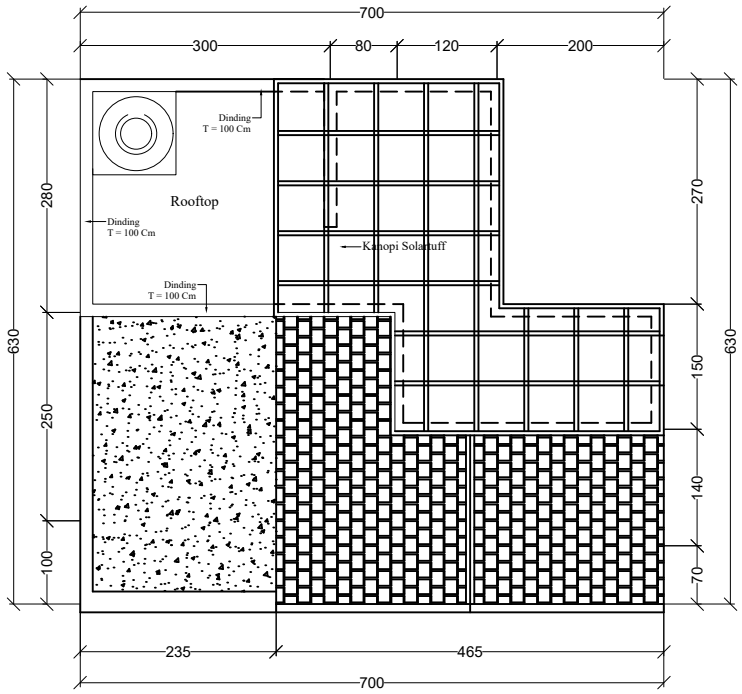

DENAH RENCANA ATAP
SKALA 1:90

SHOP DRAWING

LEGEND

OWNER

IBU IDA

CONTRACTOR

PT.GAHARU KONSTRUKSINDO UTAMA

DRAWING TITLE

DENAH RENCANA

DRAWING SCALE

1:90

PROJECT LOCATION

PULO JAHE

APPROVAL BY

PANGGAH NUZHUL RIZKI


DRAWING BY

MELA SARI FATONAH

DATE	: 07/10/2022
REVISION	: -
DRAWING CODE	: AR-003
PAGE	: 03



TAMPAK DEPAN
SKALA 1:90

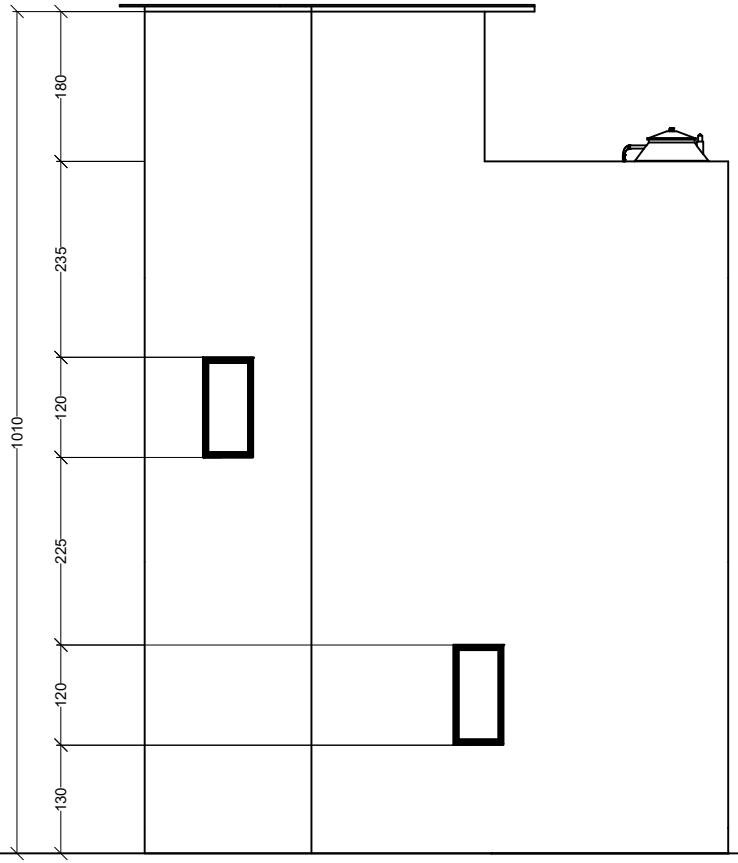

TAMPAK BELAKANG
SKALA 1:90

SHOP DRAWING

LEGEND

OWNER

IBU IDA

CONTRACTOR

PT.GAHARU KONSTRUKSINDO UTAMA

DRAWING TITLE

DENAH RENCANA

DRAWING SCALE

1:90

PROJECT LOCATION

PULO JAHE


APPROVAL BY

PANGGAH NUZHUL RIZKI


DRAWING BY

MELA SARI FATONAH

DATE	: 17/10/2022
REVISION	: -
DRAWING CODE	: AR-004
PAGE	: 04

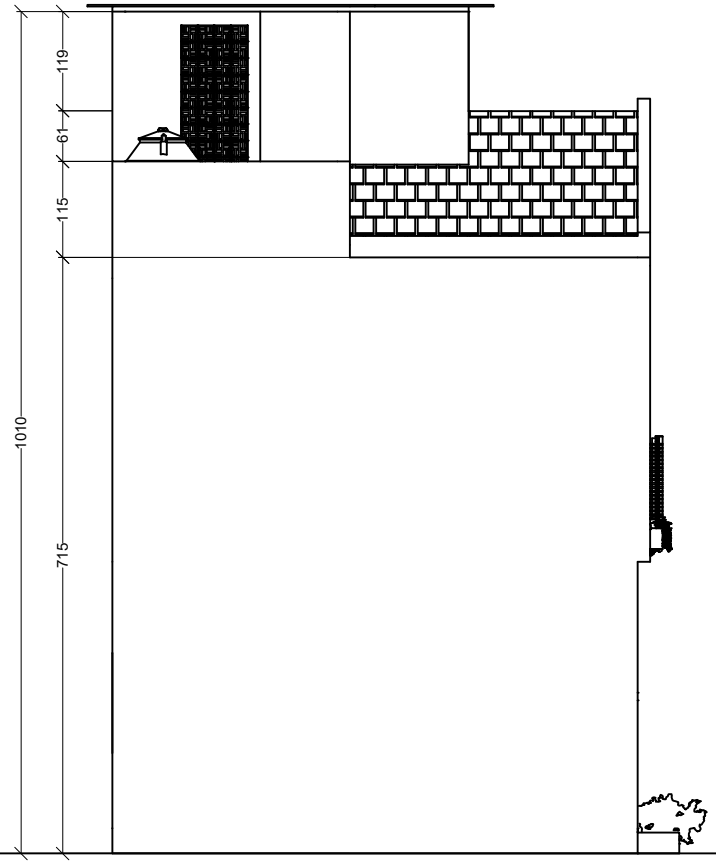

TAMPAK DEPAN
SKALA 1:90

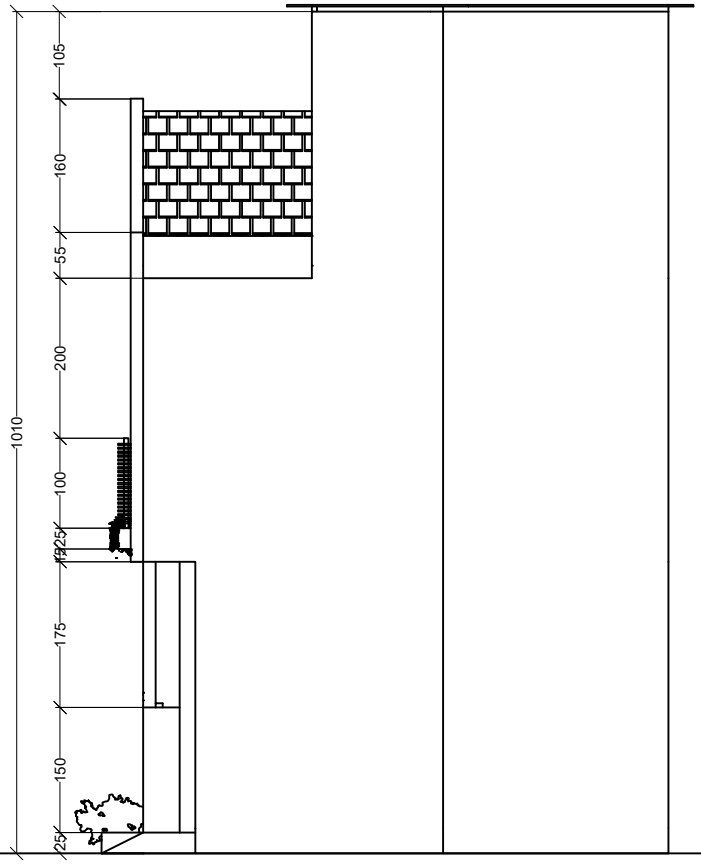

TAMPAK BELAKANG
SKALA 1:90

SHOP DRAWING

LEGEND

OWNER

IBU IDA

CONTRACTOR

PT.GAHARU KONSTRUKSINDO UTAMA

DRAWING TITLE

DENAH RENCANA

DRAWING SCALE

1:90

PROJECT LOCATION

PULO JAHE


APPROVAL BY

PANGGAH NUZHUL RIZKI


DRAWING BY

MELA SARI FATONAH

DATE	: 17/10/2022
REVISION	: -
DRAWING CODE	: AR-005
PAGE	: 05

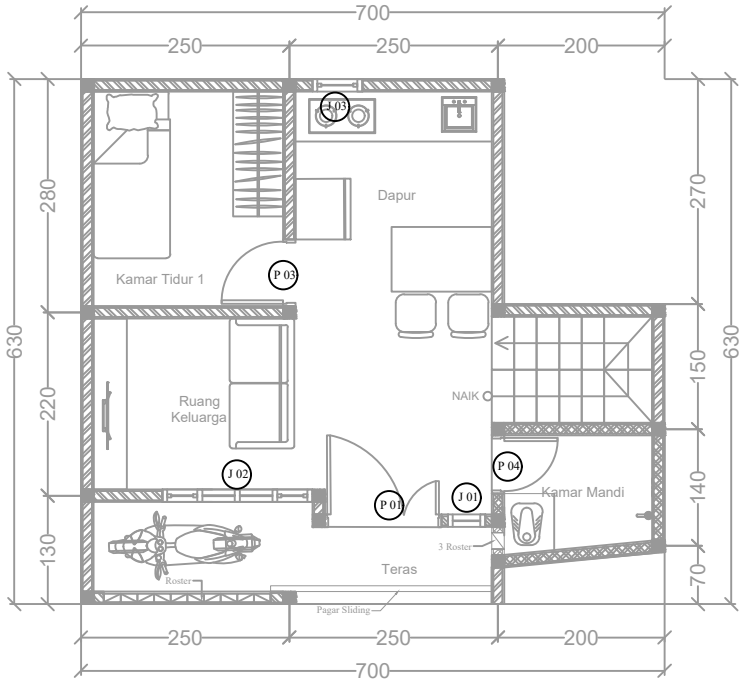


DENAH RENCANA PINTU DAN JENDELA LT. 1
SKALA 1:90

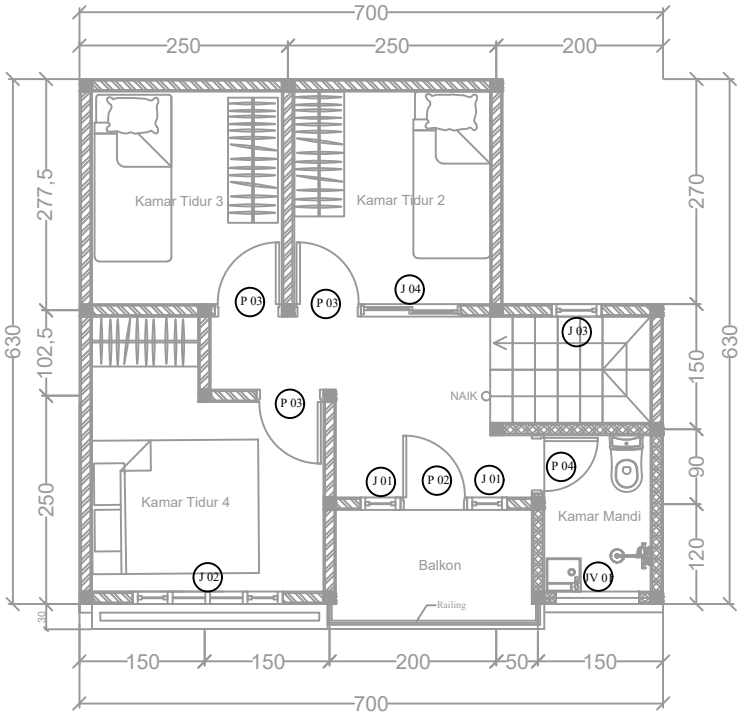

DENAH RENCANA PINTU DAN JENDELA LT. 2
SKALA 1:90

SHOP DRAWING
LEGEND
OWNER
IBU IDA
CONTRACTOR
PT.GAHARU KONSTRUKSINDO UTAMA
DRAWING TITLE
DENAH RENCANA
DRAWING SCALE
1:90
PROJECT LOCATION
PULO JAHE
APPROVAL BY
PANGGAH NUZHUL RIZKI
DRAWING BY
DYANSHA ALYYA PUTRI

DATE	: 18/10/2022
REVISION	: -
DRAWING CODE	: AR-006
PAGE	: 06

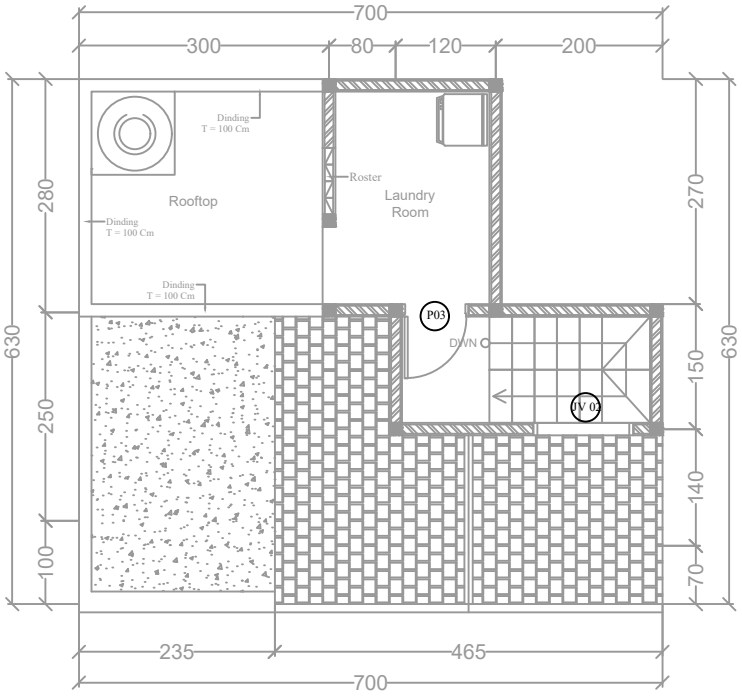

DENAH RENCANA PINTU DAN JENDELA LT. 3
SKALA 1:90

SHOP DRAWING

LEGEND

OWNER

IBU IDA

CONTRACTOR

PT.GAHARU KONSTRUKSINDO UTAMA

DRAWING TITLE

DENAH RENCANA

DRAWING SCALE

1:90

PROJECT LOCATION

PULO JAHE


APPROVAL BY

PANGGAH NUZHUL RIZKI


DRAWING BY

DYANSHA ALYYA PUTRI


DATE	: 18/10/2022
REVISION	: -
DRAWING CODE	: AR-007
PAGE	: 07

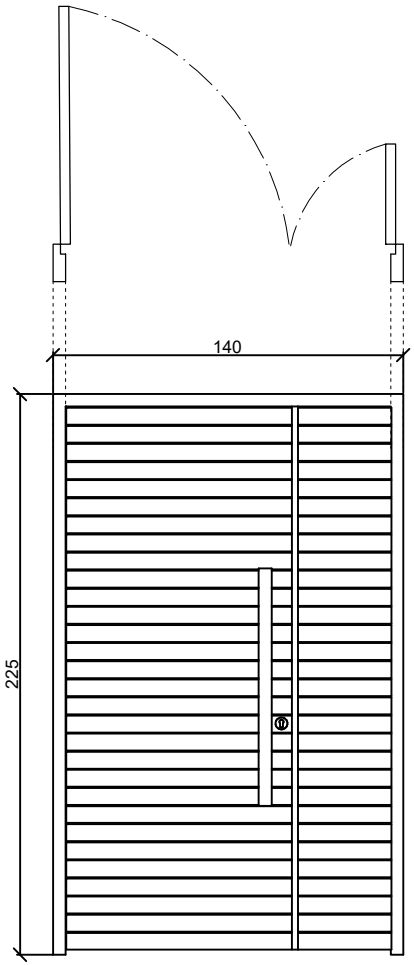


P 01
SKALA 1:40

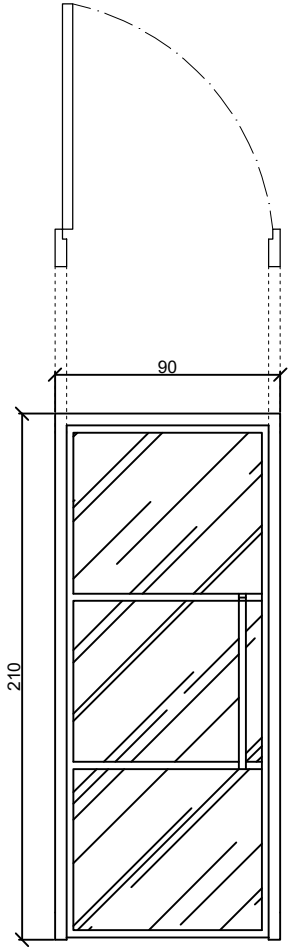

P 02
SKALA 1:40

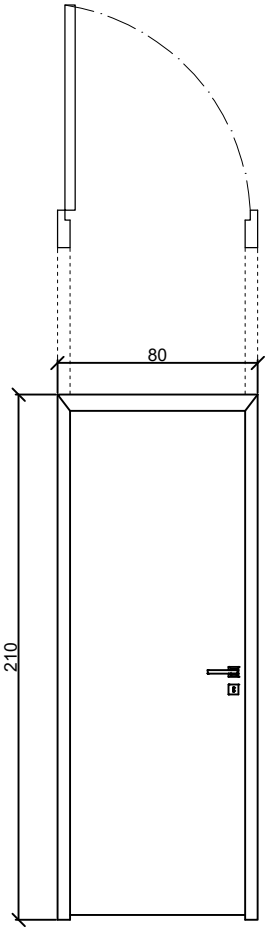

P 03
SKALA 1:40

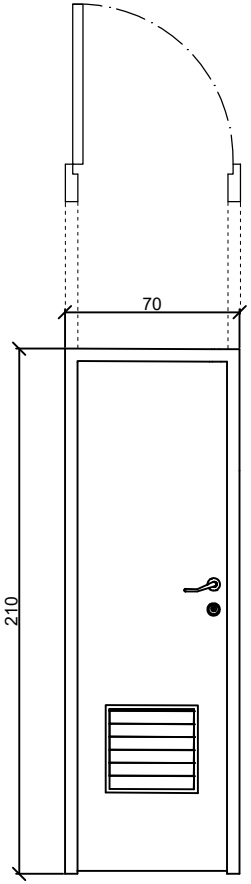

P 04
SKALA 1:40

SHOP DRAWING

LEGEND

OWNER

IBU IDA

CONTRACTOR

PT.GAHARU KONSTRUKSINDO UTAMA

DRAWING TITLE

DETAIL PINTU

DRAWING SCALE

1:40

PROJECT LOCATION

PULO JAHE


APPROVAL BY

PANGGAH NUZHUL RIZKI


DRAWING BY

MELA SARI FATONAH


DATE	: 18/10/22
REVISION	: -
DRAWING CODE	: AR-008
PAGE	: 08

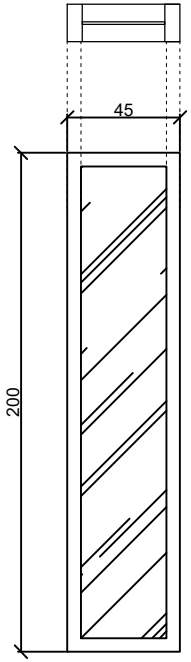


J 01
SKALA 1:40

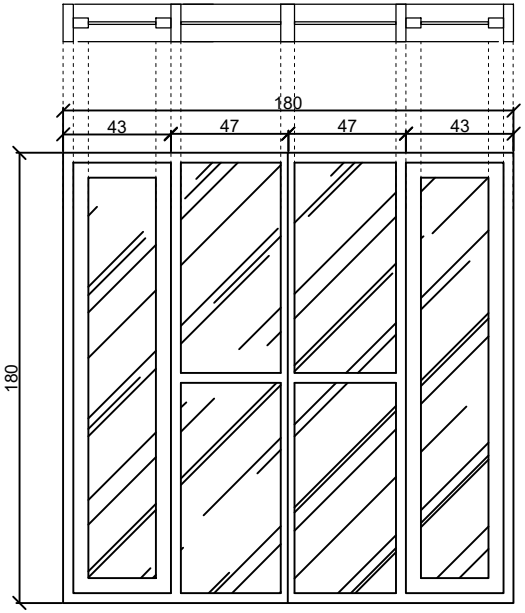


J 02
SKALA 1:40

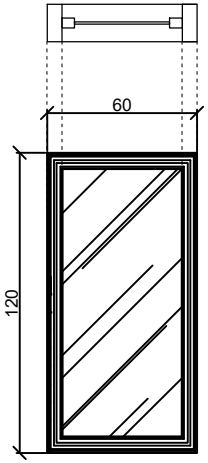


J 03
SKALA 1:40

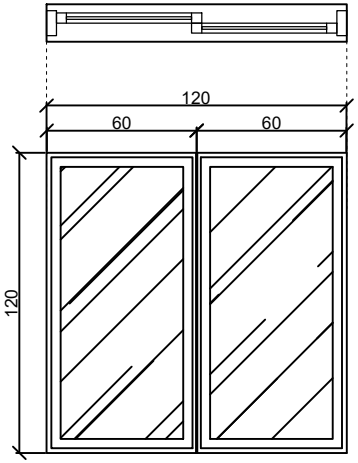

J 04
SKALA 1:40

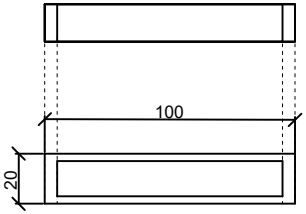

VJ 01
SKALA 1:40

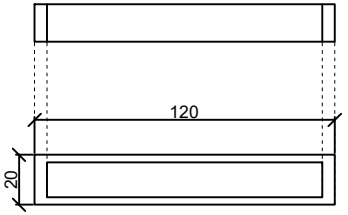

VJ 02
SKALA 1:40

SHOP DRAWING

LEGEND

OWNER

IBU IDA

CONTRACTOR

PT.GAHARU KONSTRUKSINDO UTAMA

DRAWING TITLE

DETAIL PINTU

DRAWING SCALE

1:40

PROJECT LOCATION

PULO JAHE

APPROVAL BY

PANGGAH NUZHUL RIZKI

DRAWING BY


MELA SARI FATONAH

DATE : 18/10/22


REVISION : -

DRAWING CODE : AR-009

PAGE : 09

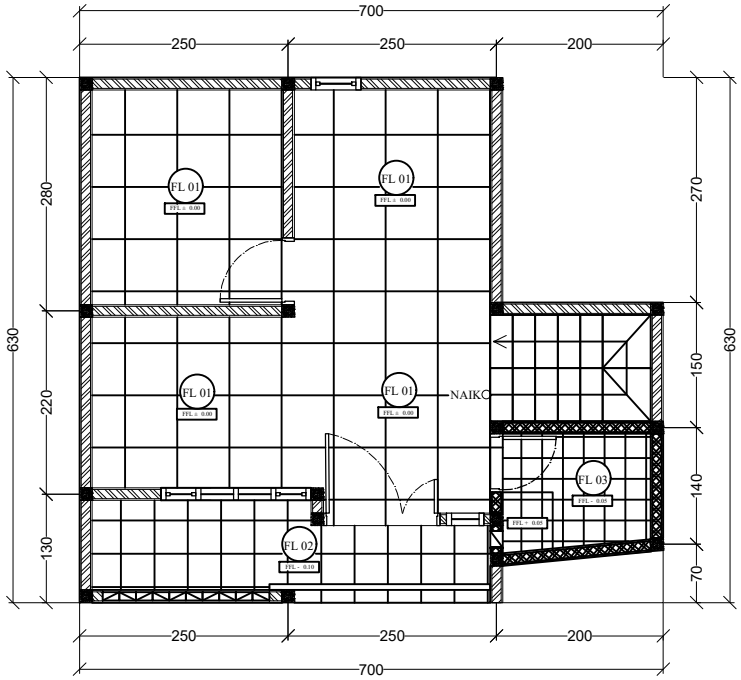

DENAH RENCANA POLA LANTAI LT. 1
SKALA 1:90

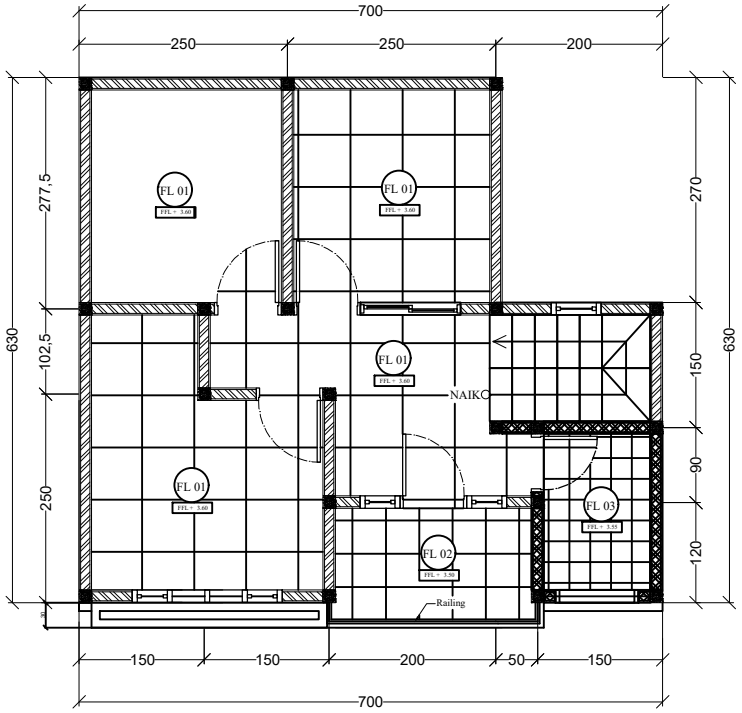

DENAH RENCANA POLA LANTAI LT. 2
SKALA 1:90

KET.	BAHAN	MOTIF	KODE	UKURAN
FL01	ROMAN GRANIT	DPLOZLANA LIGHT	GT602517R	60CM X60CM
FL02	NIRO GRANIT	LUX 3.0 ASH GREY	GT602517R	60CM X60CM
FL03	KERAMIK PLATINUM	ROMA MATT GRAY	MTA-56388747	25CM X25CM
FL04	KERAMIK SIGNATURE	EVEREST TAUFE	SI-9R-EVRS34SG	40CM X40CM

SHOP DRAWING

LEGEND

OWNER

IBU IDA

CONTRACTOR

PT.GAHARU KONSTRUKSINDO UTAMA

DRAWING TITLE

DENAH RENCANA

DRAWING SCALE

1:90

PROJECT LOCATION

PULO JAHE


APPROVAL BY

PANGGAH NUZHUL RIZKI

DRAWING BY

MELA SARI FATONAH

DATE : 19/10/2022
REVISION : -
DRAWING CODE : AR-010
PAGE : 10

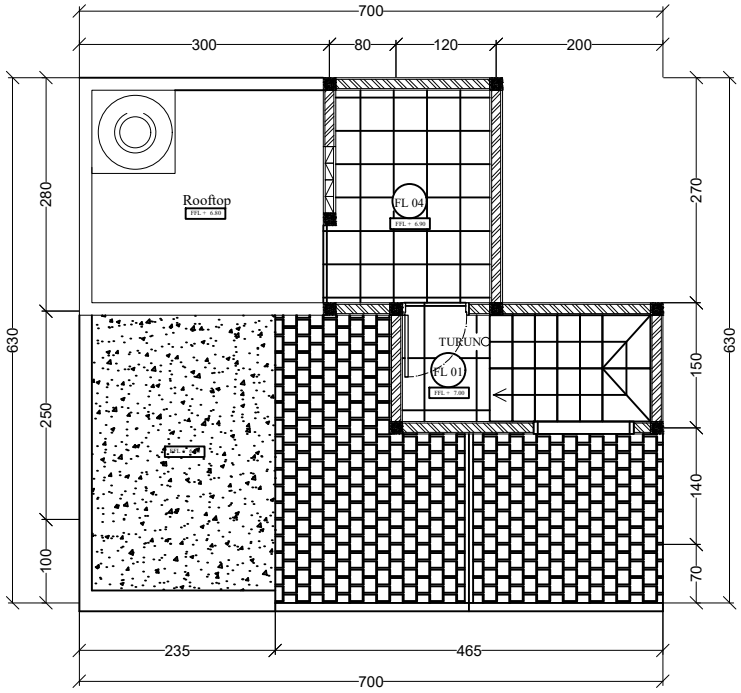

DENAH RENCANA POLA LT. 3
SKALA 1:90

KET.	BAHAN	MOTIF	KODE	UKURAN
FL01	ROMAN GRANIT	DPLOZLANA LIGHT	GT602517R	60CM X60CM
FL02	NIRO GRANIT	LUX 3.0 ASH GREY	GT602517R	60CM X60CM
FL03	KERAMIK PLATINUM	ROMA MATT GRAY	MTA-56388747	25CM X25CM
FL04	KERAMIK SIGNATURE	EVEREST TAUFE	SI-9R-EVRS34SG	40CM X40CM

SHOP DRAWING

LEGEND

OWNER

IBU IDA

CONTRACTOR

PT.GAHARU KONSTRUKSINDO UTAMA

DRAWING TITLE

DENAH RENCANA

DRAWING SCALE

1:90

PROJECT LOCATION

PULO JAHE


APPROVAL BY

PANGGAH NUZHUL RIZKI


DRAWING BY

MELA SARI FATONAH

DATE : 19/10/2022
REVISION : -
DRAWING CODE : AR-011
PAGE : 11

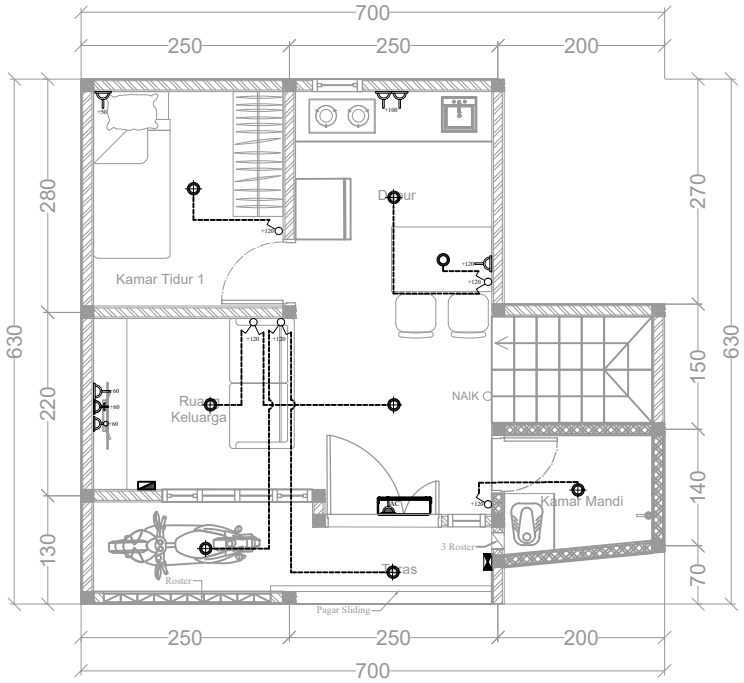

DENAH RENCANA KELISTRIKAN LT. 1
SKALA 1:90

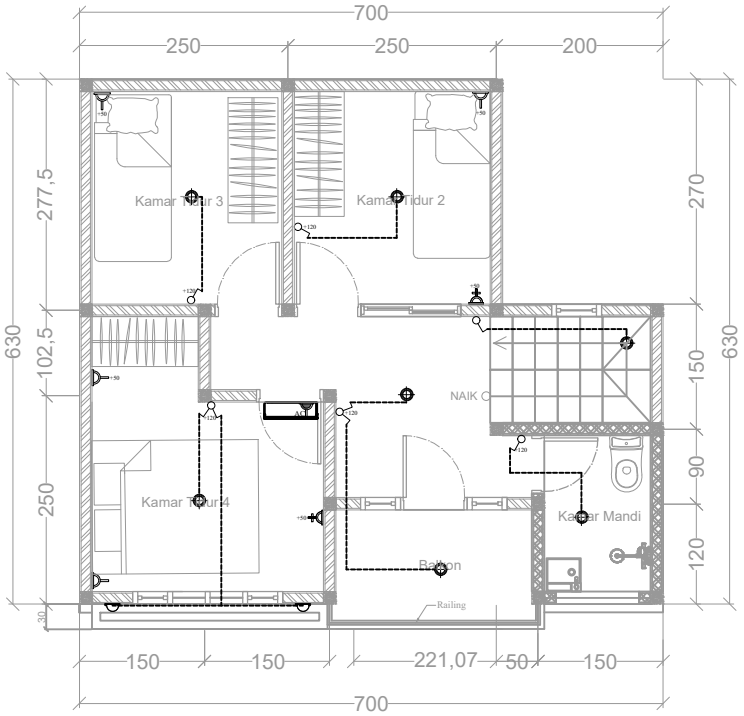

DENAH RENCANA KELISTRIKAN LT. 2
SKALA 1:90

SHOP DRAWING

LEGEND

	STOP KONTAK
	LAMPU OUTBOW
	STOP KONTAK AC
	SAKLAR SINGLE
	SAKLAR DOUBLE
	LAMPU DINDING
	LAMPU DOWNLIGHT
	STOP KONTAK TV
	STOP KONTAK INTERNET
	MCB
	KWH
	LAMPU GANTUNG

OWNER

IBU IDA

CONTRACTOR

PT.GAHARU KONSTRUKSINDO UTAMA

DRAWING TITLE

DENAH RENCANA

DRAWING SCALE

1:90

PROJECT LOCATION

PULO JAHE


APPROVAL BY

PANGGAH NUZHUL RIZKI

DRAWING BY

DYANSHA ALYYA PUTRI

DATE	: 17/10/2022
REVISION	: -
DRAWING CODE	: ME-001
PAGE	: 12

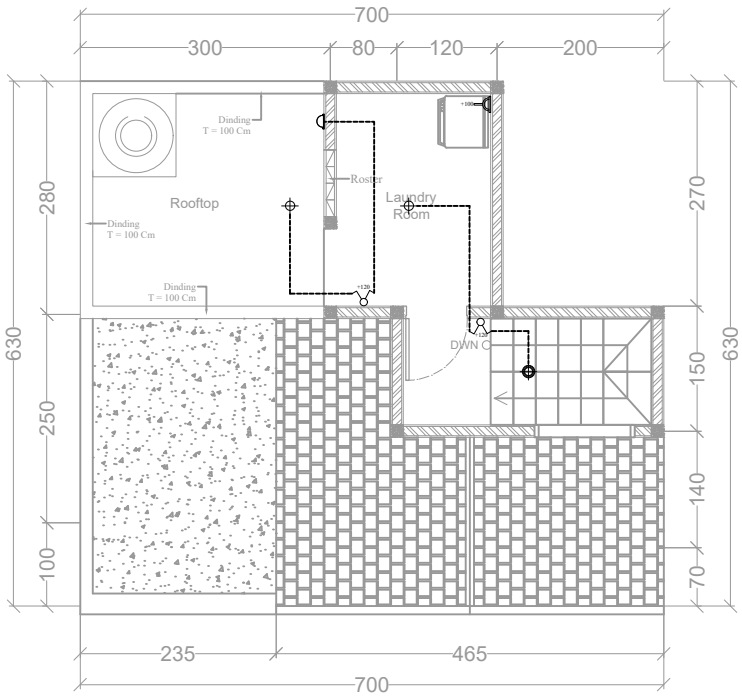

DENAH RENCANA KELISTRIKAN LT. 3
SKALA 1:90

SHOP DRAWING

LEGEND

	STOP KONTAK
	LAMPU OUTBOW
	STOP KONTAK AC
	SAKLAR SINGLE
	SAKLAR DOUBLE
	LAMPU DINDING
	LAMPU DOWNLIGHT
	STOP KONTAK TV
	STOP KONTAK INTERNET
	MCB
	KWH

OWNER

IBU IDA

CONTRACTOR

PT.GAHARU KONSTRUKSINDO UTAMA

DRAWING TITLE

DENAH RENCANA

DRAWING SCALE

1:90

PROJECT LOCATION

PULO JAHE


APPROVAL BY

PANGGAH NUZHUL RIZKI


DRAWING BY

DYANSHA ALYYA PUTRI

DATE	: 17/10/2022
REVISION	: -
DRAWING CODE	: ME-002
PAGE	: 13

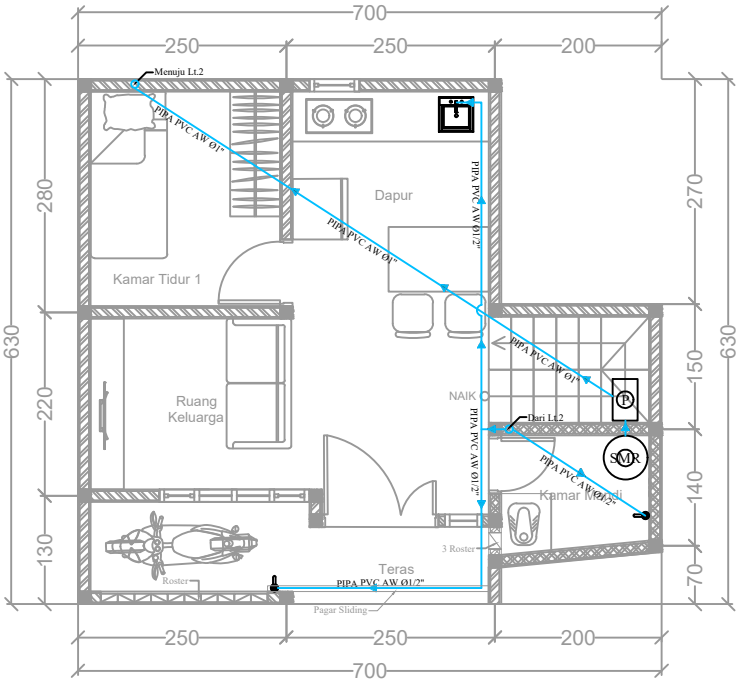

DENAH RENCANA AIR BERSIH LT. 1
SKALA 1:90

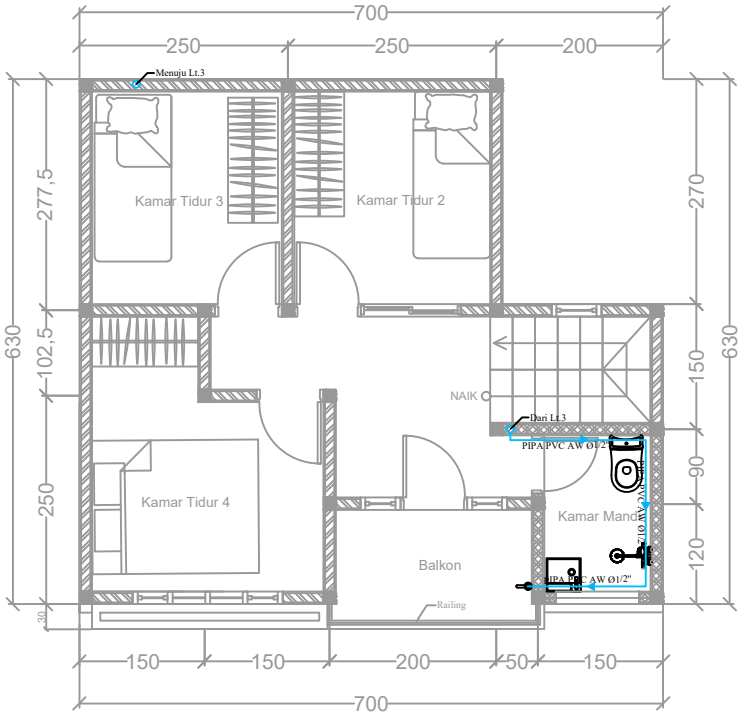

DENAH RENCANA AIR BERSIH LT. 2
SKALA 1:90

SHOP DRAWING

LEGEND

	JALUR AIR
	SUMUR
	PIPA AIR BERSIH
	KRAN
	SHOWER
	POMPA

OWNER

IBU IDA

CONTRACTOR

PT.GAHARU KONSTRUKSINDO UTAMA

DRAWING TITLE

DENAH RENCANA

DRAWING SCALE

1:90

PROJECT LOCATION

PULO JAHE


APPROVAL BY

PANGGAH NUZHUL RIZKI

DRAWING BY

MELA SARI FATONAH

DATE	: 17/10/2022
REVISION	: -
DRAWING CODE	: PLM-001
PAGE	: 14

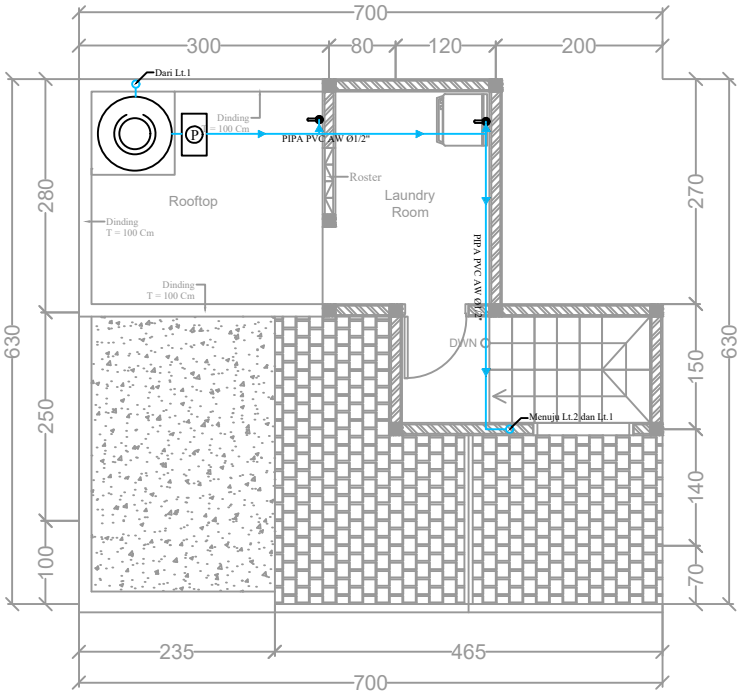

DENAH RENCANA AIR BERSIH LT. 3
SKALA 1:90

SHOP DRAWING

LEGEND

	JALUR AIR
	SUMUR
	PIPA AIR BERSIH
	KRAN
	SHOWER
	POMPA

OWNER

IBU IDA

CONTRACTOR

PT.GAHARU KONSTRUKSINDO UTAMA

DRAWING TITLE

DENAH RENCANA

DRAWING SCALE

1:90

PROJECT LOCATION

PULO JAHE


APPROVAL BY

PANGGAH NUZHUL RIZKI


DRAWING BY

MELA SARI FATONAH

DATE	: 17/10/2022
REVISION	: -
DRAWING CODE	: PLM-002
PAGE	: 15

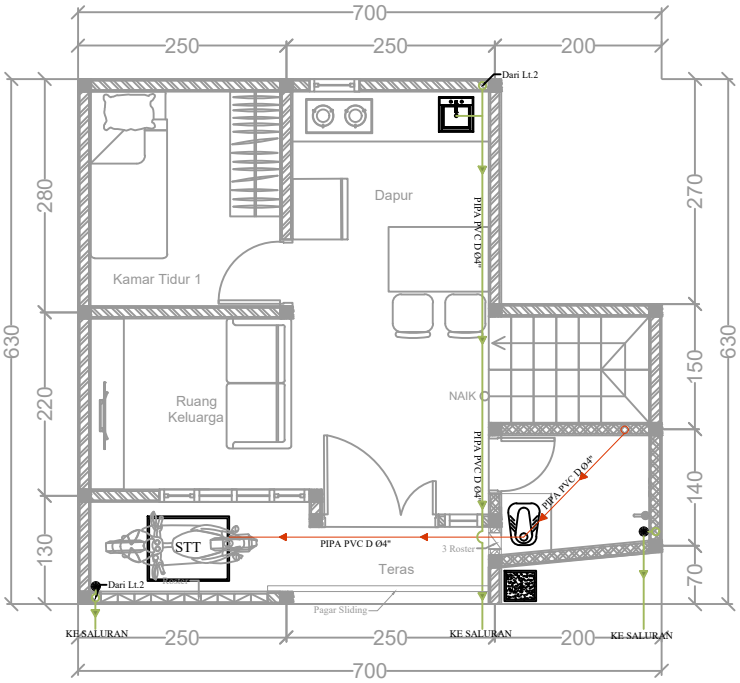

DENAH RENCANA AIR KOTOR LT. 1
SKALA 1:90

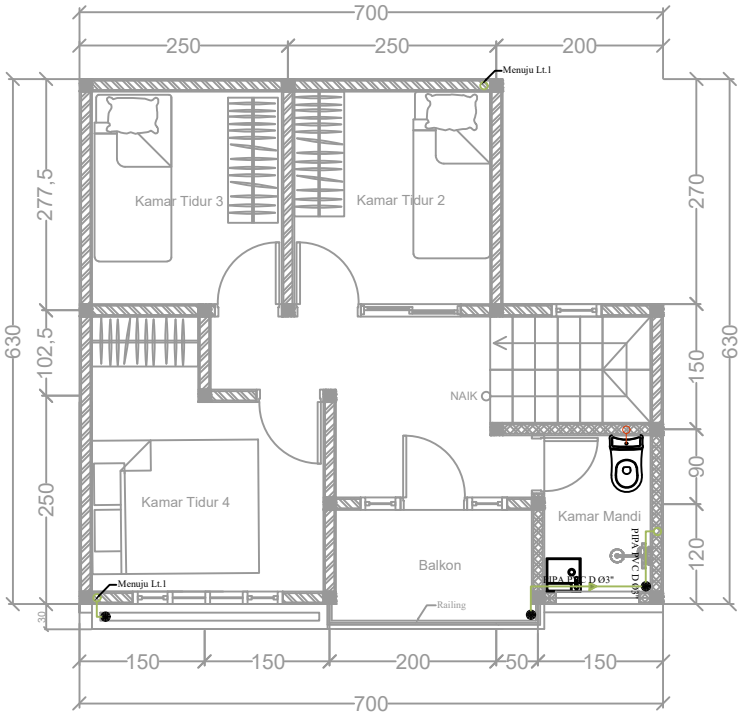

DENAH RENCANA AIR KOTOR LT. 2
SKALA 1:90

SHOP DRAWING

LEGEND

	PIPA AIR KOTOR
	FLOOR DRAIN
	PIPA AIR BEKAS
STT	SEPTIC TANK
	BAK KONTROL
	JALUR AIR BEKAS
	JALUR AIR KOTOR

OWNER

IBU IDA

CONTRACTOR

PT.GAHARU KONSTRUKSINDO UTAMA

DRAWING TITLE

DENAH RENCANA

DRAWING SCALE

1:90

PROJECT LOCATION

PULO JAHE


APPROVAL BY

PANGGAH NUZHUL RIZKI

DRAWING BY

MELA SARI FATONAH


DATE	: 17/10/2022
REVISION	: -
DRAWING CODE	: PLM-003
PAGE	: 16

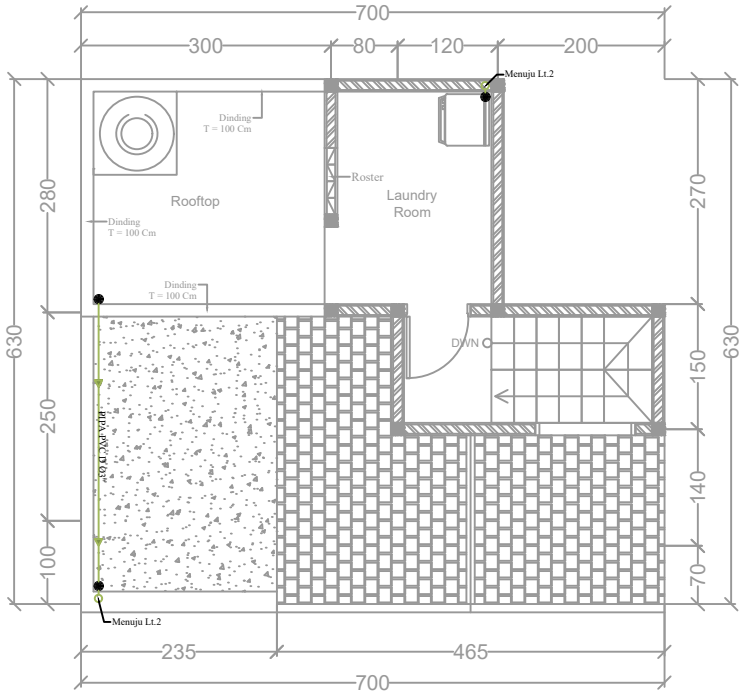

DENAH RENCANA AIR KOTOR LT. 3
SKALA 1:90

SHOP DRAWING
LEGEND
OWNER
IBU IDA
CONTRACTOR
PT.GAHARU KONSTRUKSINDO UTAMA
DRAWING TITLE
DENAH RENCANA
DRAWING SCALE
1:90
PROJECT LOCATION
PULO JAHE
APPROVAL BY
PANGGAH NUZHUL RIZKI
DRAWING BY
MELA SARI FATONAH

DATE	: 17/10/2022
REVISION	: -
DRAWING CODE	: PLM-004
PAGE	: 17

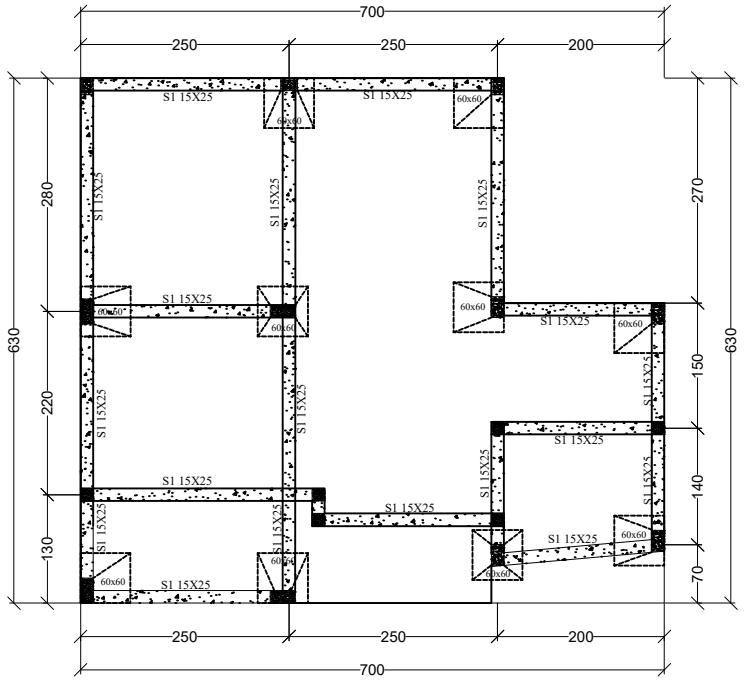

DENAH RENCANA SLOOF DAN PONDASI
SKALA 1:90

SHOP DRAWING

LEGEND

OWNER

IBU IDA

CONTRACTOR

PT.GAHARU KONSTRUKSINDO UTAMA

DRAWING TITLE

DENAH RENCANA

DRAWING SCALE

1:90

PROJECT LOCATION

PULO JAHE


APPROVAL BY

PANGGAH NUZHUL RIZKI



DRAWING BY

MELA SARI FATONAH

DATE	: 10/10/2022
REVISION	: -
DRAWING CODE	: STR-001
PAGE	: 18

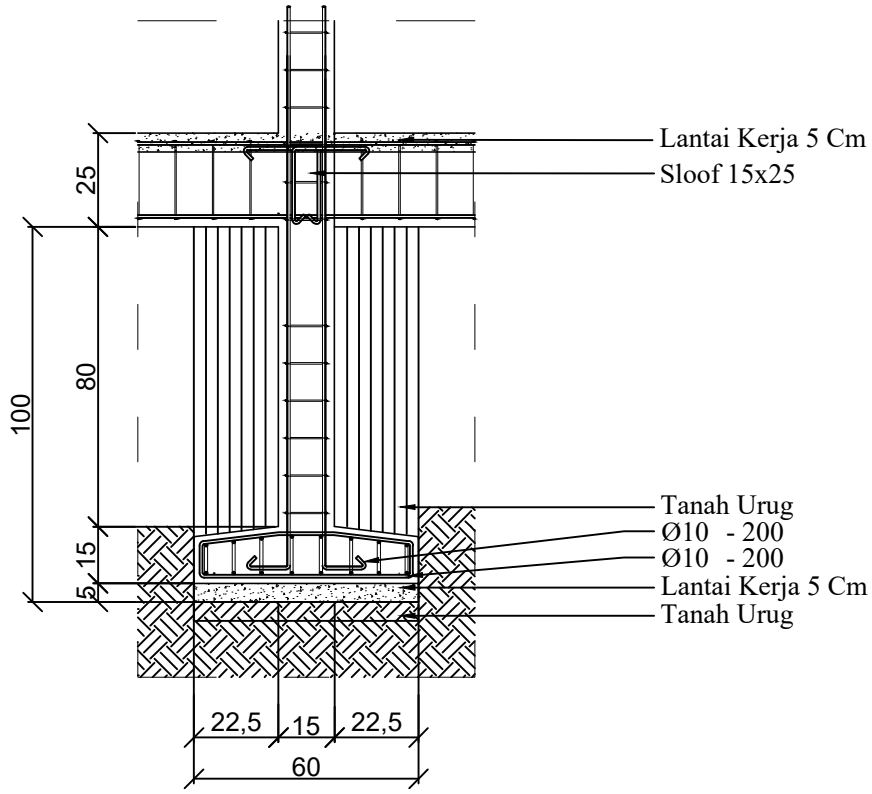

DETAIL PONDASI FOOTPLAT
SKALA 1:20

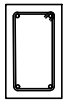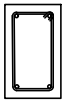KODE	S1	
POSISI	TUMPUAN	LAPANGAN
PENAMPANG		
DIMENSION	150 X 250	
TULANGAN UTAMA	4Ø12	
SENGKANG	Ø8 - 150	Ø8 - 150

TABEL PENULANGAN SLOOF
SKALA 1:20

SHOP DRAWING

LEGEND

OWNER

IBU IDA

CONTRACTOR

PT.GAHARU KONSTRUKSINDO UTAMA

DRAWING TITLE

DETAIL PENULANGAN

DRAWING SCALE

1:25

PROJECT LOCATION

PULO JAHE


APPROVAL BY

PANGGAH NUZHUL RIZKI


DRAWING BY

MELA SARI FATONAH

DATE : 18/10/22
REVISION : -
DRAWING CODE : STR-002
PAGE : 19

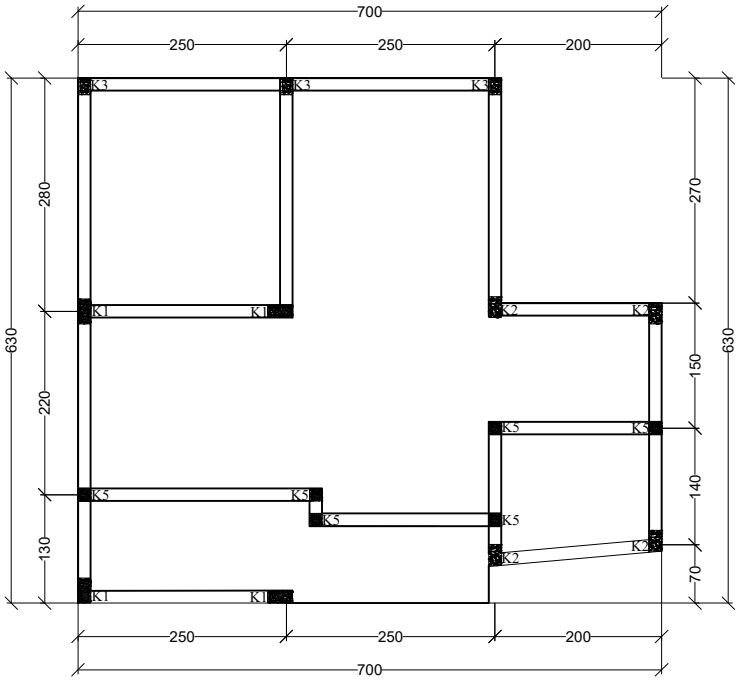

DENAH RENCANA KOLOM LT. 1
SKALA 1:90

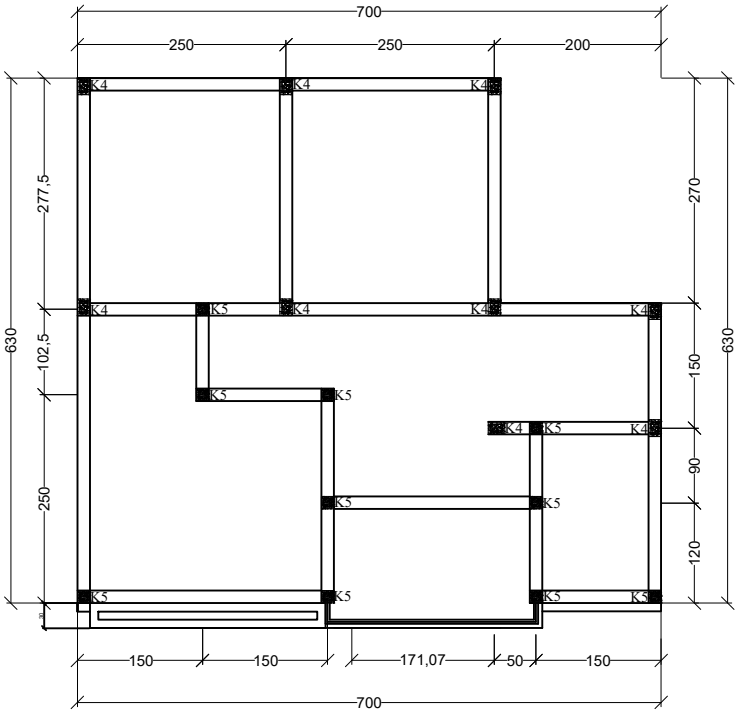

DENAH RENCANA KOLOM LT. 2
SKALA 1:90

SHOP DRAWING

LEGEND

OWNER

IBU IDA

CONTRACTOR

PT.GAHARU KONSTRUKSINDO UTAMA

DRAWING TITLE

DENAH RENCANA

DRAWING SCALE

1:90

PROJECT LOCATION

PULO JAHE


APPROVAL BY

PANGGAH NUZHUL RIZKI

DRAWING BY

MELA SARI FATONAH

DATE	: 19/10/2022
REVISION	: -
DRAWING CODE	: STR-003
PAGE	: 20

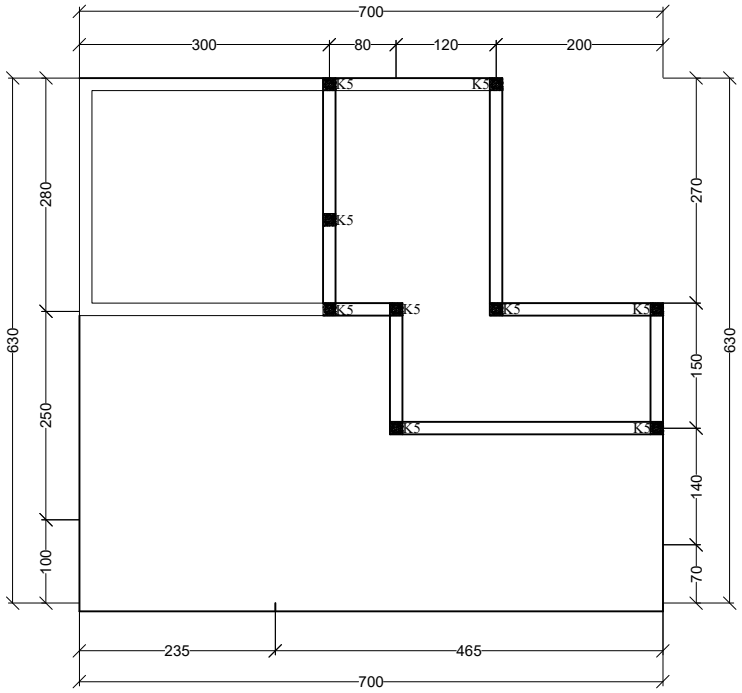

DENAH RENCANA KOLOM LT. 3
SKALA 1:90

SHOP DRAWING

LEGEND

OWNER

IBU IDA

CONTRACTOR

PT.GAHARU KONSTRUKSINDO UTAMA

DRAWING TITLE

DENAH RENCANA

DRAWING SCALE

1:90

PROJECT LOCATION

PULO JAHE


APPROVAL BY

PANGGAH NUZHUL RIZKI


DRAWING BY

MELA SARI FATONAH

DATE	: 19/10/2022
REVISION	: -
DRAWING CODE	: STR-004
PAGE	: 21

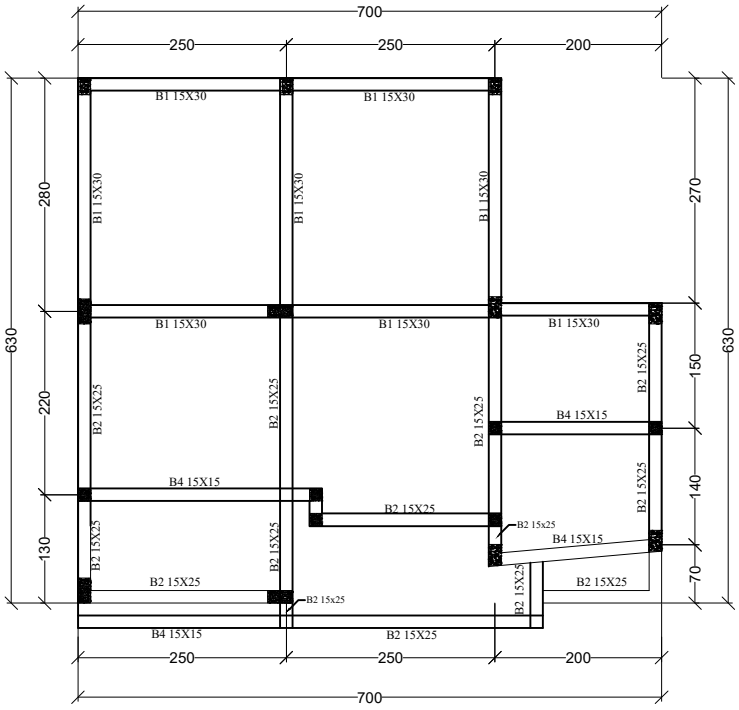

DENAH RENCANA BALOK LT. 1
SKALA 1:90

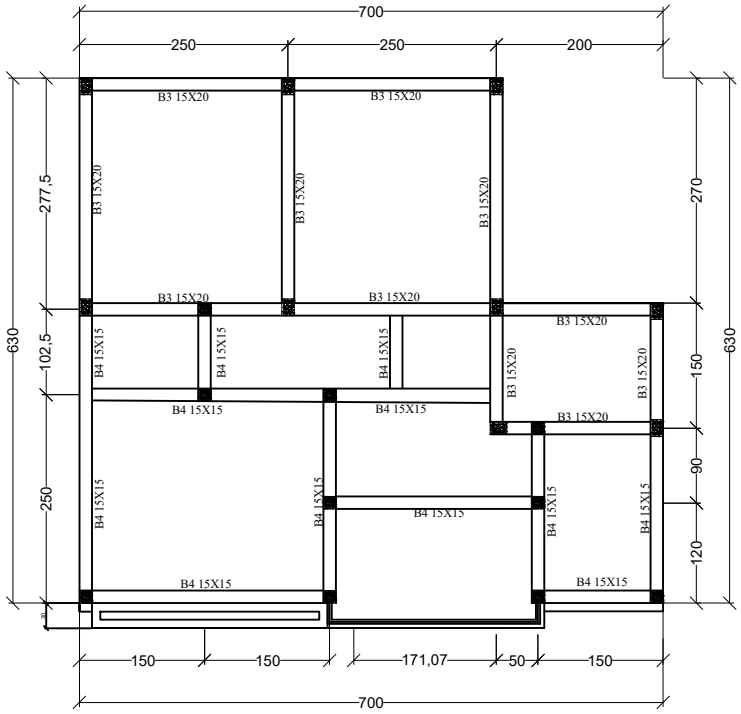

DENAH RENCANA BALOK LT. 2
SKALA 1:90

SHOP DRAWING

LEGEND

OWNER

IBU IDA

CONTRACTOR

PT.GAHARU KONSTRUKSINDO UTAMA

DRAWING TITLE

DENAH RENCANA

DRAWING SCALE

1:90

PROJECT LOCATION

PULO JAHE


APPROVAL BY

PANGGAH NUZHUL RIZKI

DRAWING BY

MELA SARI FATONAH

DATE	: 18/10/2022
REVISION	: -
DRAWING CODE	: STR-005
PAGE	: 22

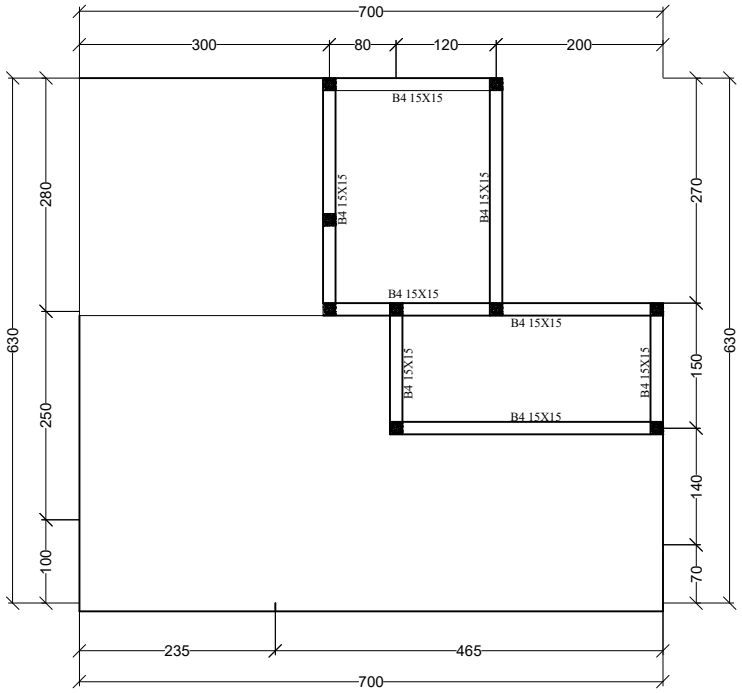

DENAH RENCANA BALOK LT. 3
SKALA 1:90

SHOP DRAWING

LEGEND

OWNER

IBU IDA

CONTRACTOR

PT.GAHARU KONSTRUKSINDO UTAMA

DRAWING TITLE

DENAH RENCANA

DRAWING SCALE

1:90

PROJECT LOCATION

PULO JAHE

APPROVAL BY

PANGGAH NUZHUL RIZKI

DRAWING BY

MELA SARI FATONAH

DATE	: 18/10/2022
REVISION	: -
DRAWING CODE	: STR-006
PAGE	: 23

KODE	K1		K2		K3		K4		K5	
POSISI	END SECTION	MID SECTION	TUMPUAN	LAPANGAN	END SECTION	MID SECTION	END SECTION	MID SECTION	END SECTION	MID SECTION
PENAMPANG										
DIMENSION	150 X 300		150 X 250		150 X 200		150 X 200		150 X 150	
TULANGAN UTAMA	6Ø12		6Ø12		6D13		6Ø12		4Ø8	
SENGKANG	Ø8 - 150	Ø8 - 150	Ø8 - 150	Ø8 - 150	Ø8 - 150	Ø8 - 150	Ø8 - 150	Ø8 - 150	Ø8 - 150	Ø8 - 150

TABEL PENULANGAN KOLOM
SKALA 1:40

KODE	B1		B2		B3		B4	
POSISI	TUMPUAN	LAPANGAN	TUMPUAN	LAPANGAN	TUMPUAN	LAPANGAN	TUMPUAN	LAPANGAN
PENAMPANG								
DIMENSION	150 X 300		150 X 250		150 X 200		150 X 200	
TULANGAN UTAMA	6Ø12		6Ø12		6Ø10		4Ø10	
SENGKANG	Ø8 - 150	Ø8 - 150	Ø8 - 150	Ø8 - 150	Ø8 - 150	Ø8 - 150	Ø8 - 150	Ø8 - 150

TABEL PENULANGAN BALOK
SKALA 1:40

SHOP DRAWING

LEGEND

OWNER

IBU TIYA

CONTRACTOR

PT.GAHARU KONSTRUKSINDO UTAMA

DRAWING TITLE

DETAIL PINTU

DRAWING SCALE

1:40

PROJECT LOCATION

JATI ASIH

APPROVAL BY

PANGGAH NUZHUL RIZKI

DRAWING BY


MELA SARI FATONAH

DATE : 18/10/22


REVISION : -

DRAWING CODE : STR-007

PAGE : 24

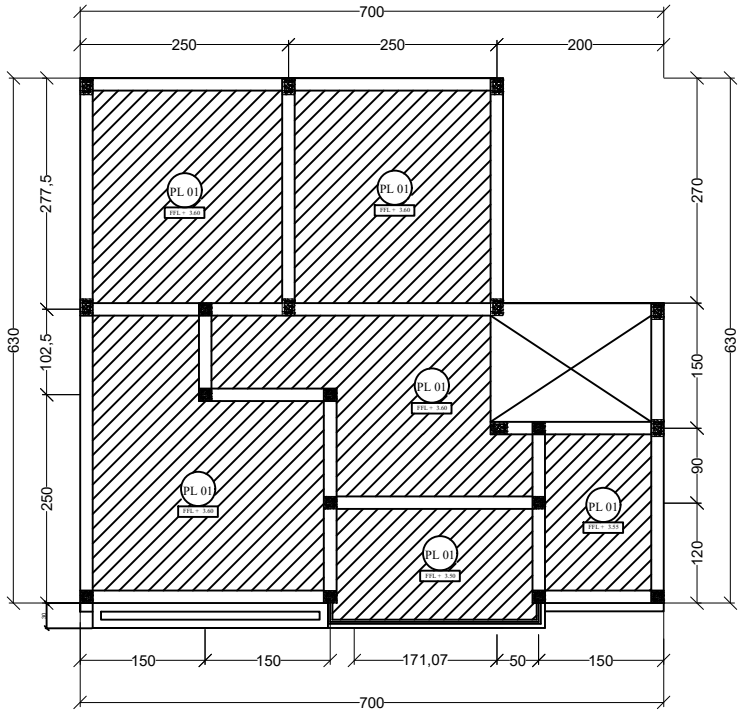

DENAH RENCANA PLAT LANTAI LT. 2
SKALA 1:90

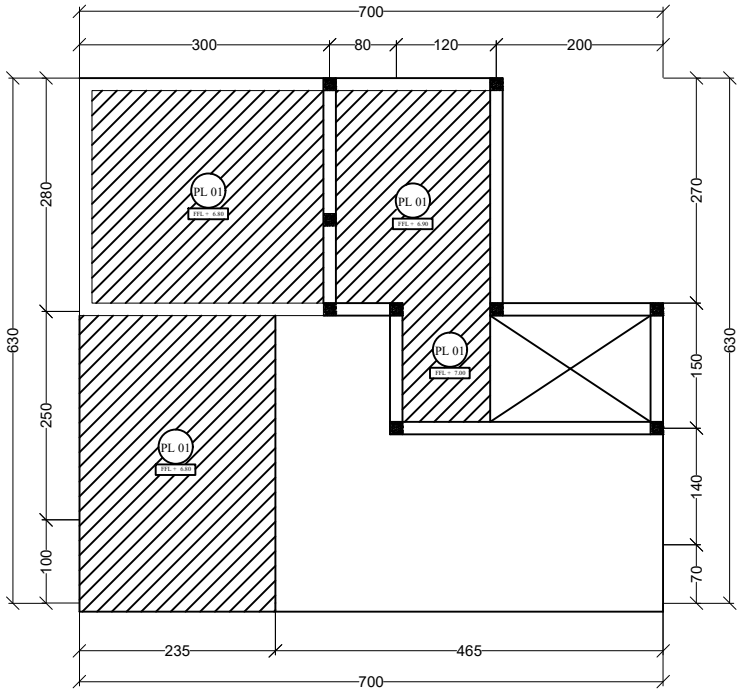

DENAH RENCANA PLAT LANTAI LT. 3
SKALA 1:90

SHOP DRAWING

LEGEND

OWNER

IBU IDA

CONTRACTOR

PT.GAHARU KONSTRUKSINDO UTAMA

DRAWING TITLE

DENAH RENCANA

DRAWING SCALE

1:90

PROJECT LOCATION

PULO JAHE


APPROVAL BY


PANGGAH NUZHUL RIZKI

DRAWING BY

MELA SARI FATONAH

DATE	: 18/10/2022
REVISION	: -
DRAWING CODE	: STR-008
PAGE	: 25

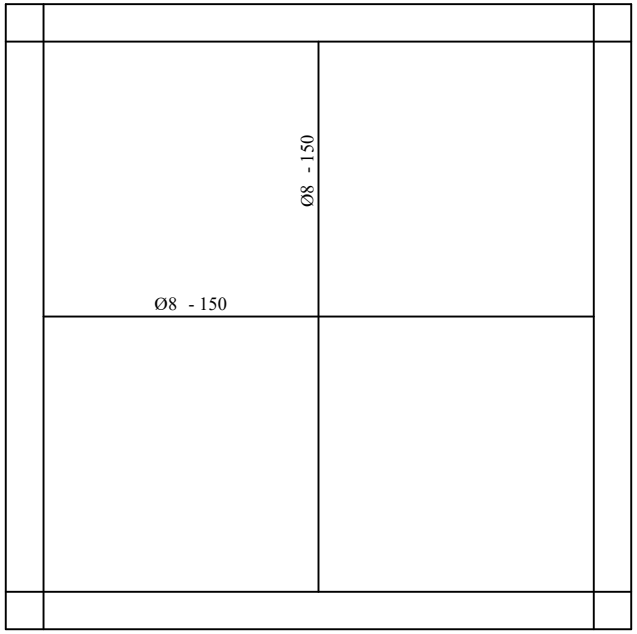

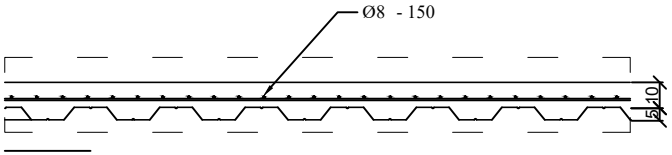

DETAIL PLAT LANTAI P1
SKALA 1:40

SHOP DRAWING

LEGEND

OWNER

IBU IDA

CONTRACTOR

PT.GAHARU KONSTRUKSINDO UTAMA

DRAWING TITLE

DETAIL PINTU

DRAWING SCALE

1:40

PROJECT LOCATION

PULO JAHE


APPROVAL BY

PANGGAH NUZHUL RIZKI

DRAWING BY

MELA SARI FATONAH

DATE : 18/10/22
REVISION : -
DRAWING CODE : STR-009
PAGE : 26

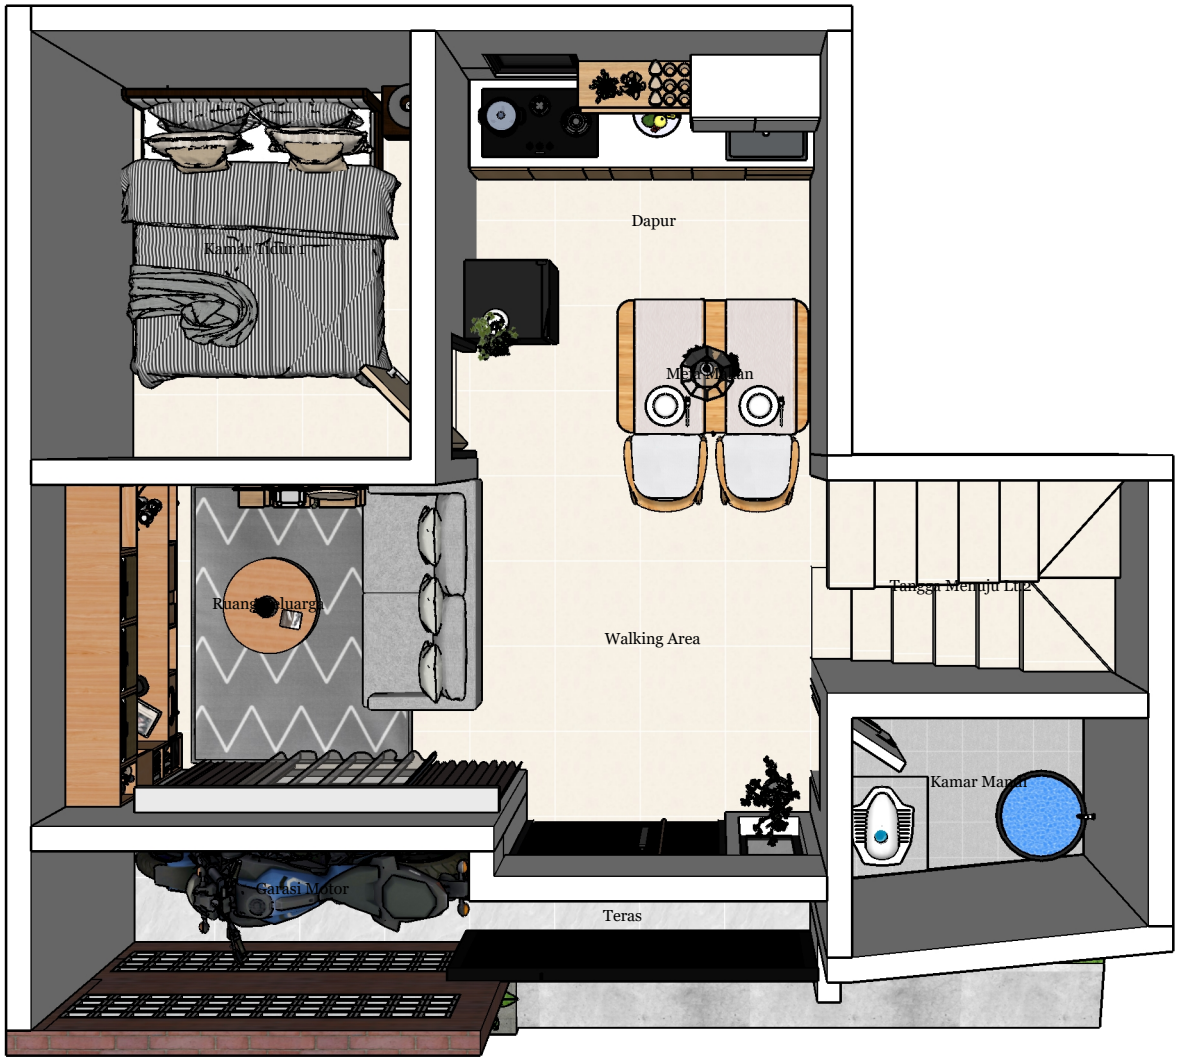

DENAH RENCANA Lt.1 3D

GAHARU KONSTRUKSINDO UTAMA @renovasirumah_minimalis (+62) 811-9409-368	Project : RUMAH	Drawing By : Mela Sari Fatonah, S.Ars	REVISIONS		AR-012
	Owner: IBU IDA	Approval By : Panggah Nuzhulrizky, S.T	MM/DD/YY / REMARKS		
	Drawing Title : DENAH RENCANA Lt.1 3D	Scale : / Date : 29/09/2022	1 __/__/__ ...		
		File Name : / Print Date :	2 __/__/__ ...		
			3 __/__/__ ...		
			4 __/__/__ ...		27
			5 __/__/__ ...		



DENAH RENCANA LT.2 3D

GAHARU KONSTRUKSINDO UTAMA
@renovasirumah_minimalis
(+62) 811-9409-368

Project : RUMAH	Drawing By : Mela Sari Fatonah, S.Ars	REVISIONS	AR-013
Owner: IBU IDA	Approval By : Panggah Nuzhulrizky, S.T		
Drawing Title : DENAH RENCANA LT.2 3D	Scale : / Date : 29/09/2022		
	File Name : / Print Date :		28

	MM/DD/YY	REMARKS
1	__/__/__	...
2	__/__/__	...
3	__/__/__	...
4	__/__/__	...
5	__/__/__	...



DENAH RENCANA LT.3 3D

GAHARU KONSTRUKSINDO UTAMA
@renovasirumah_minimalis
(+62) 811-9409-368

Project : RUMAH	Drawing By : Mela Sari Fatonah, S.Ars	REVISIONS	AR-014
Owner: IBU IDA	Approval By : Panggah Nuzhulrizky, S.T		
Drawing Title : DENAH RENCANA LT.3 3D	Scale : / Date : 29/09/2022		
	File Name : / Print Date :		

	MM/DD/YY	REMARKS
1	__/__/__	...
2	__/__/__	...
3	__/__/__	...
4	__/__/__	...
5	__/__/__	...



DENAH RENCANA ATAP 3D

GAHARU KONSTRUKSINDO UTAMA
@renovasirumah_minimalis
(+62) 811-9409-368

Project : RUMAH	Drawing By : Mela Sari Fatonah, S.Ars		
Owner: IBU IDA	Approval By : Panggah Nuzhulrizky, S.T		
Drawing Title : DENAH RENCANA ATAP 3D	Scale :	Date : 29/09/2022	
	File Name :	Print Date :	

REVISIONS		
	MM/DD/YY	REMARKS
1	__/__/__	...
2	__/__/__	...
3	__/__/__	...
4	__/__/__	...
5	__/__/__	...

AR-015


ANR95

